
NOTES / LEGEND

W1 Aluminium window 1.50 x 1.40, sill +0.90 above slab, thermal-break profile, RAL 7016
D1 Entrance door, double leaf 2.40 x 2.60, aluminium + laminated glass 6.6.2
CW-1 Stick curtain wall 4.00 x 9.40, mullions 50x150 @ 1.00, transoms @ 1.57
Balcony railings: aluminium vertical balusters @ 0.20, h=1.05
All dimensions in metres. Check on site before fabrication.

N

חזית דרומית
SOUTH ELEVATION

SCALE 1:100

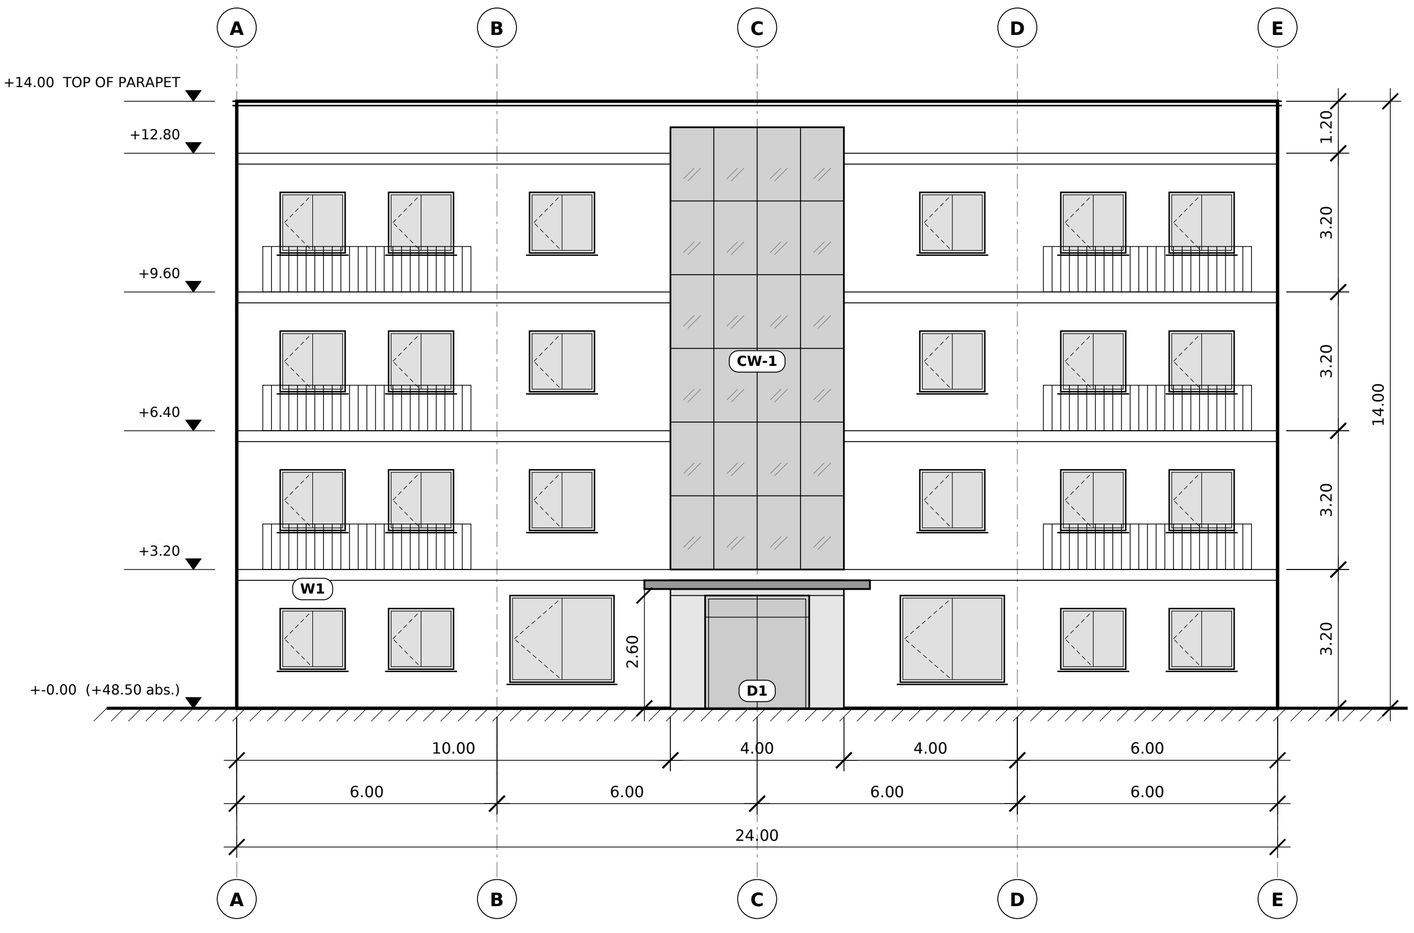

0 2 4 6 8 10 m SCALE 1:100

DEMO

Sample sheet for aluminium takeoff app

ARCHITECT / ALUMINIUM CONSULTANT
Demo Architects Studio | Facade & Aluminium Works

PROJECT
HADAR RESIDENCE - BUILDING 3 פרויקט הדר

DRAWING TITLE
SOUTH ELEVATION **חזית דרומית**

UNITS **metres**	STATUS **DEMO / NOT FOR CONSTRUCTION**
DRAWN **R. Levi**	CHECKED **M. Cohen**
DATE **2026-10-15**	REVISION **B - for tender**
SCALE **1:100**	PAPER **A2 594 x 420 mm**
SHEET **1 / 3**	DRAWING NO. **A-301**


NOTES / LEGEND

CW-2 Stair core curtain wall 3.00 x 13.40, full height, mullions @ 1.00
W2 Ribbon window module 1.50 x 1.20, fixed + tilt/turn alternating
D2 Service door 1.20 x 2.20, aluminium insulated panel
D3 Refuse room double door 3.00 x 2.95, louvred aluminium
All dimensions in metres. Check on site before fabrication.

N

חזית צפונית
NORTH ELEVATION

SCALE 1:100

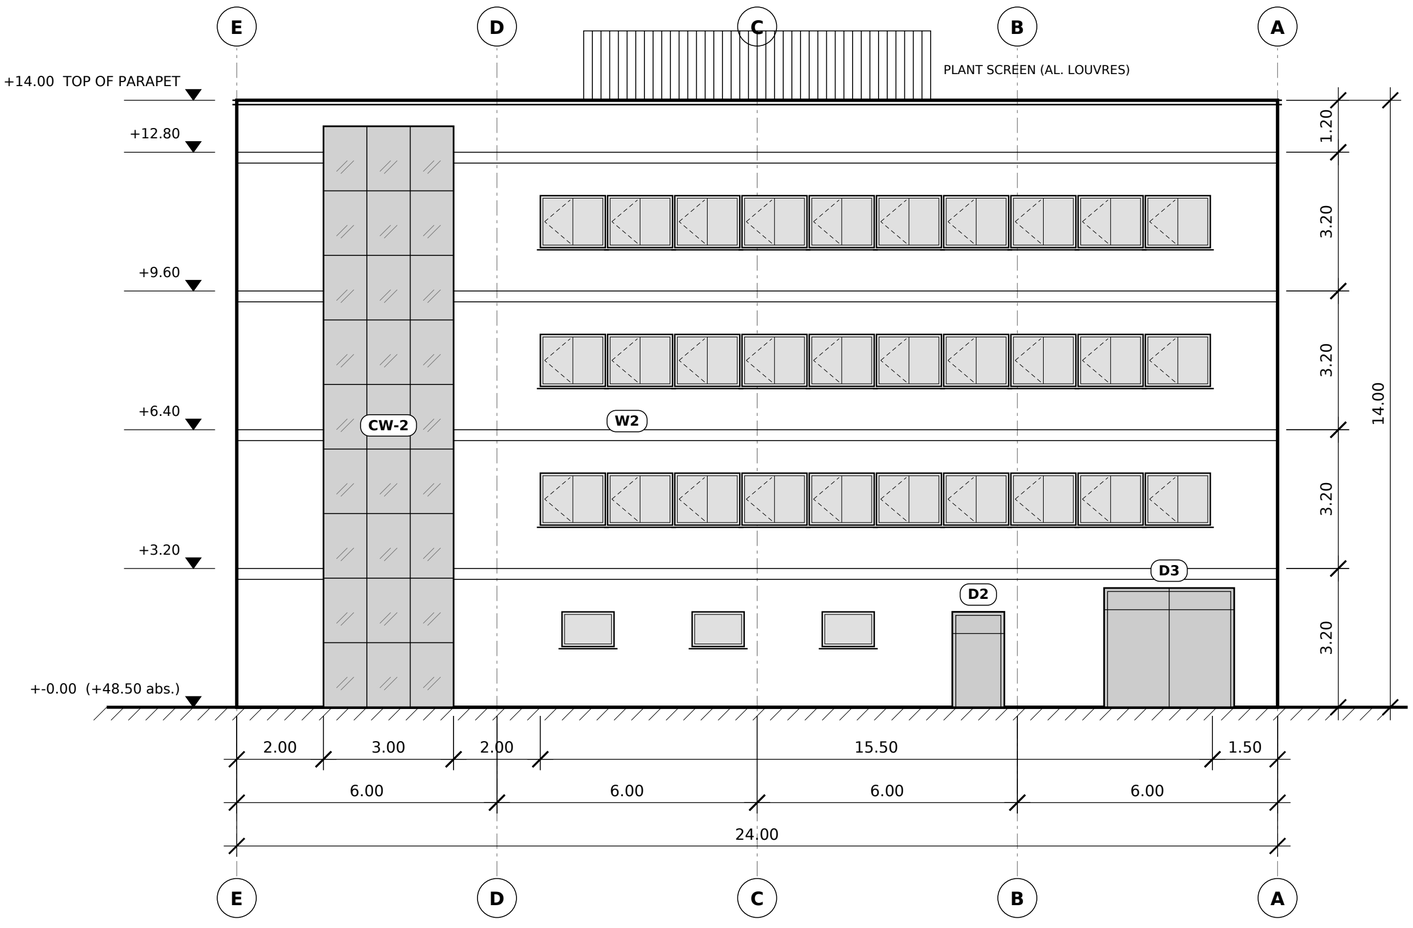

0 2 4 6 8 10 m SCALE 1:100

DEMO

Sample sheet for aluminium takeoff app

ARCHITECT / ALUMINIUM CONSULTANT
Demo Architects Studio | Facade & Aluminium Works

PROJECT
HADAR RESIDENCE - BUILDING 3 פרויקט הדר


DRAWING TITLE
NORTH ELEVATION **חזית צפונית**

UNITS **metres**	STATUS **DEMO / NOT FOR CONSTRUCTION**
DRAWN **R. Levi**	CHECKED **M. Cohen**
DATE **2026-10-15**	REVISION **B - for tender**
SCALE **1:100**	PAPER **A2 594 x 420 mm**
SHEET **2 / 3**	DRAWING NO. **A-302**

N

תוכנית קומת קרקע
GROUND FLOOR PLAN

SCALE 1:100

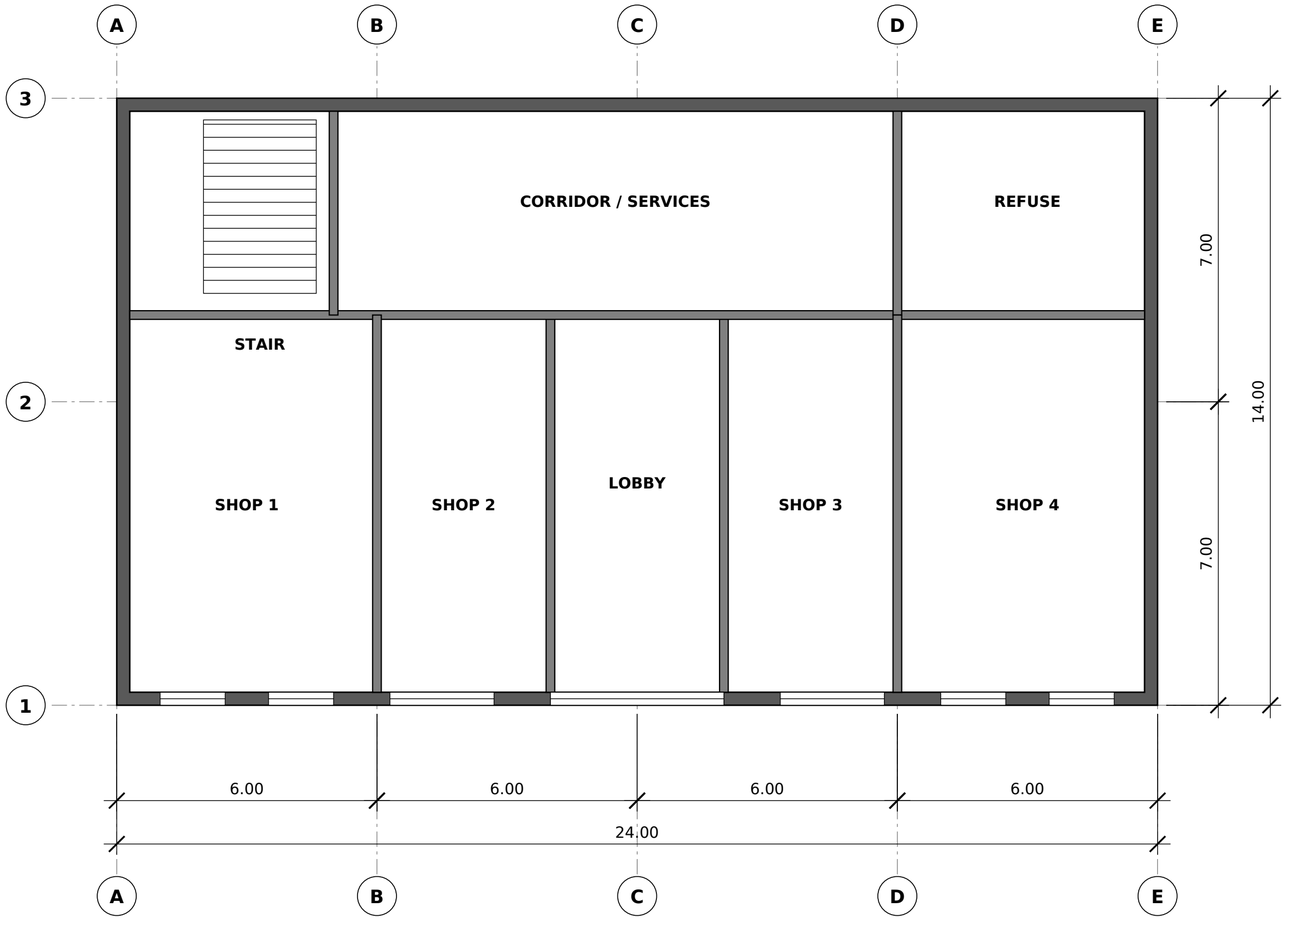

0 2 4 6 8 10 m SCALE 1:100

DEMO

Sample sheet for aluminium takeoff app

ARCHITECT / ALUMINIUM CONSULTANT

Demo Architects Studio | Facade & Aluminium Works

PROJECT

HADAR RESIDENCE - BUILDING 3 פרויקט הדר

DRAWING TITLE

GROUND FLOOR PLAN **תוכנית קרקע**

UNITS **metres**	STATUS **DEMO / NOT FOR CONSTRUCTION**
DRAWN **R. Levi**	CHECKED **M. Cohen**
DATE **2026-10-15**	REVISION **B - for tender**
SCALE **1:100**	PAPER **A2 594 x 420 mm**
SHEET **3 / 3**	DRAWING NO. **A-101**